



PLANTA

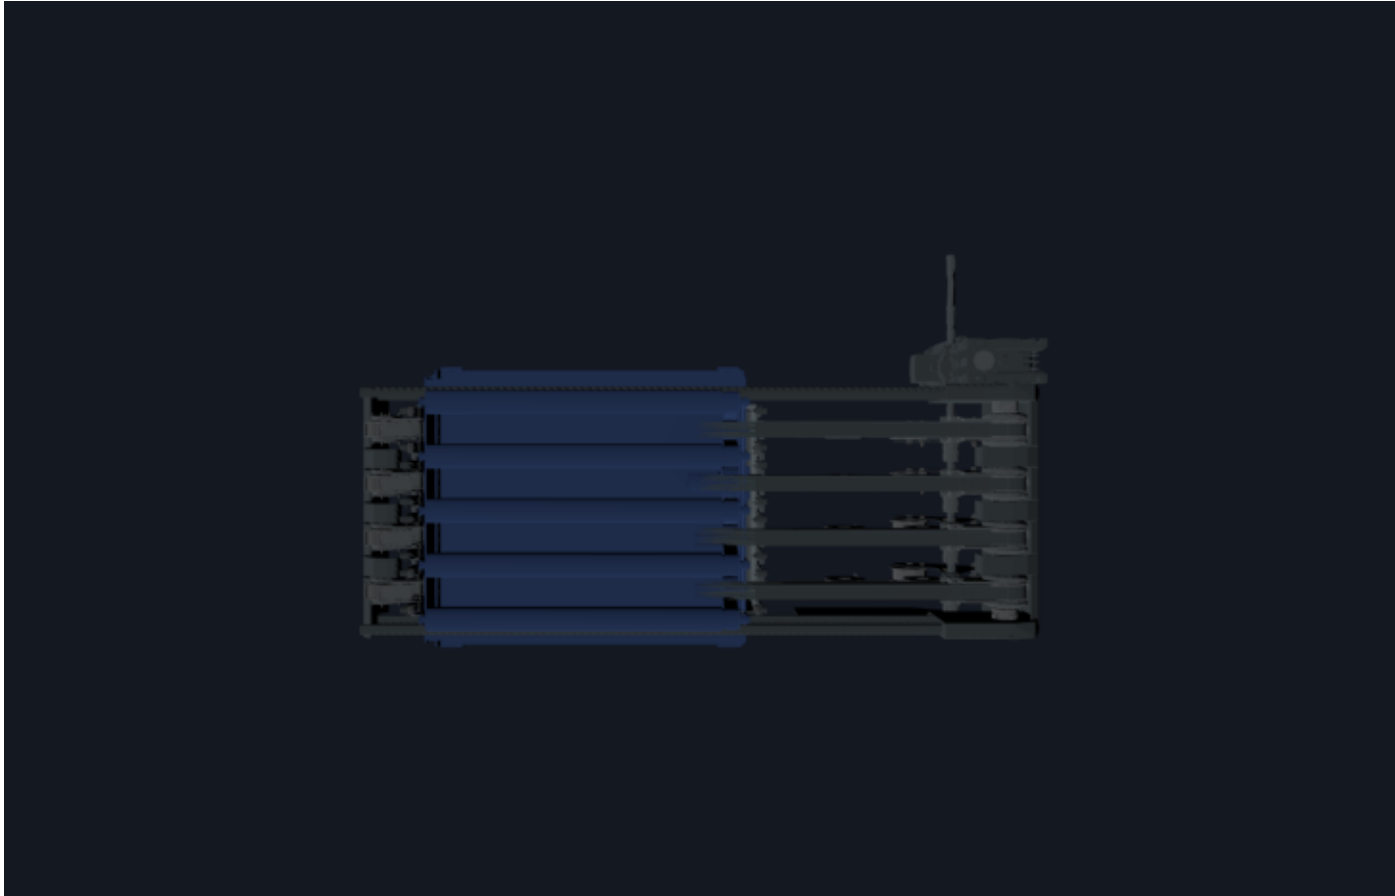

ALZADO

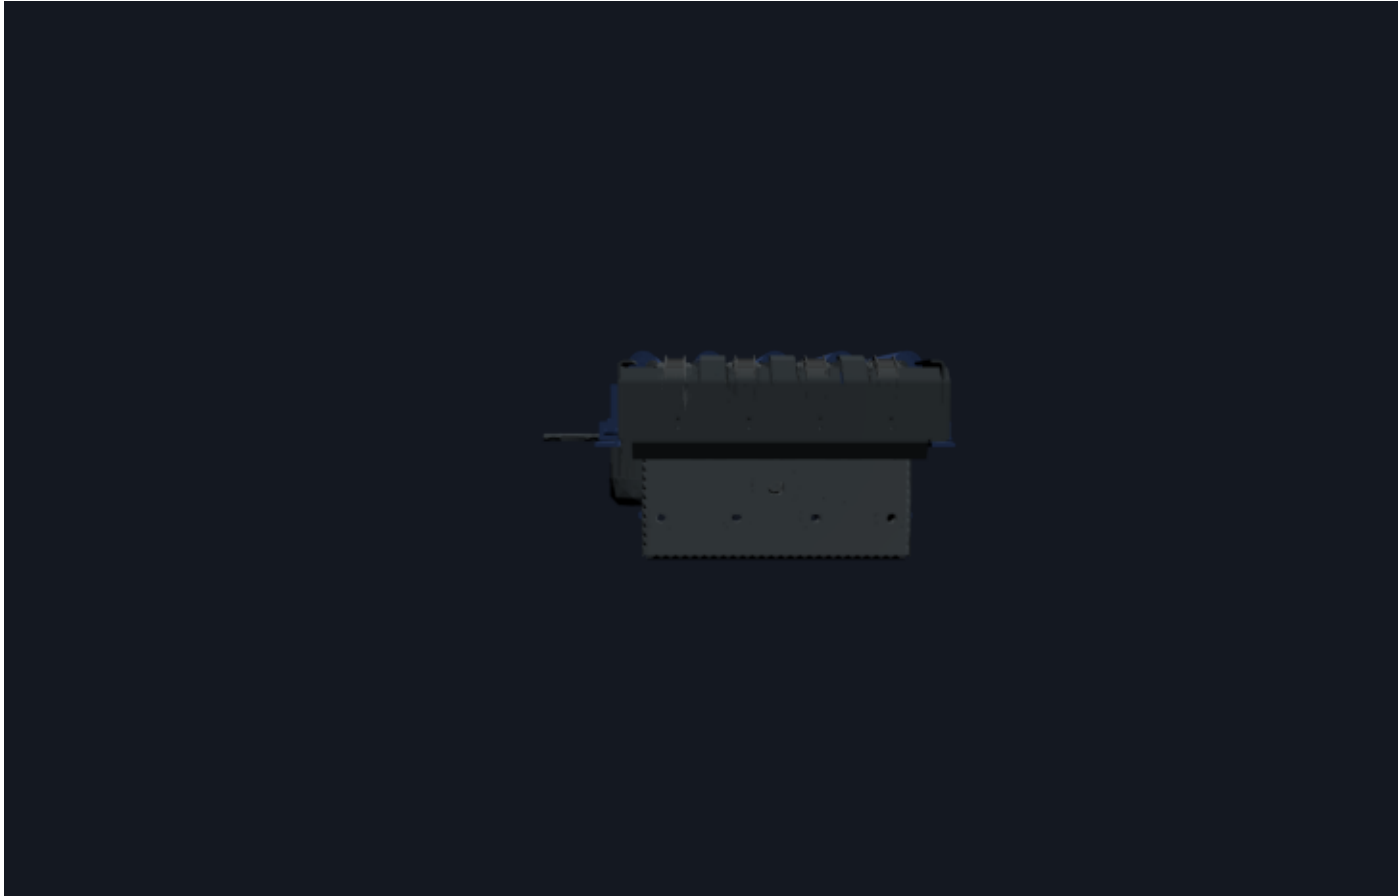

PERFIL



ISOMÉTRICA



FOTOGRAFÍA

SORTER REAL (sorter_CO.stp) + Transferencia 90°

Vistas ortográficas (1er diedro) + isométrica

Escala s/e (vista sombreada) · mm · 2026-07-20

Corte longitudinal A-A (plano X=208, eje de máquina)

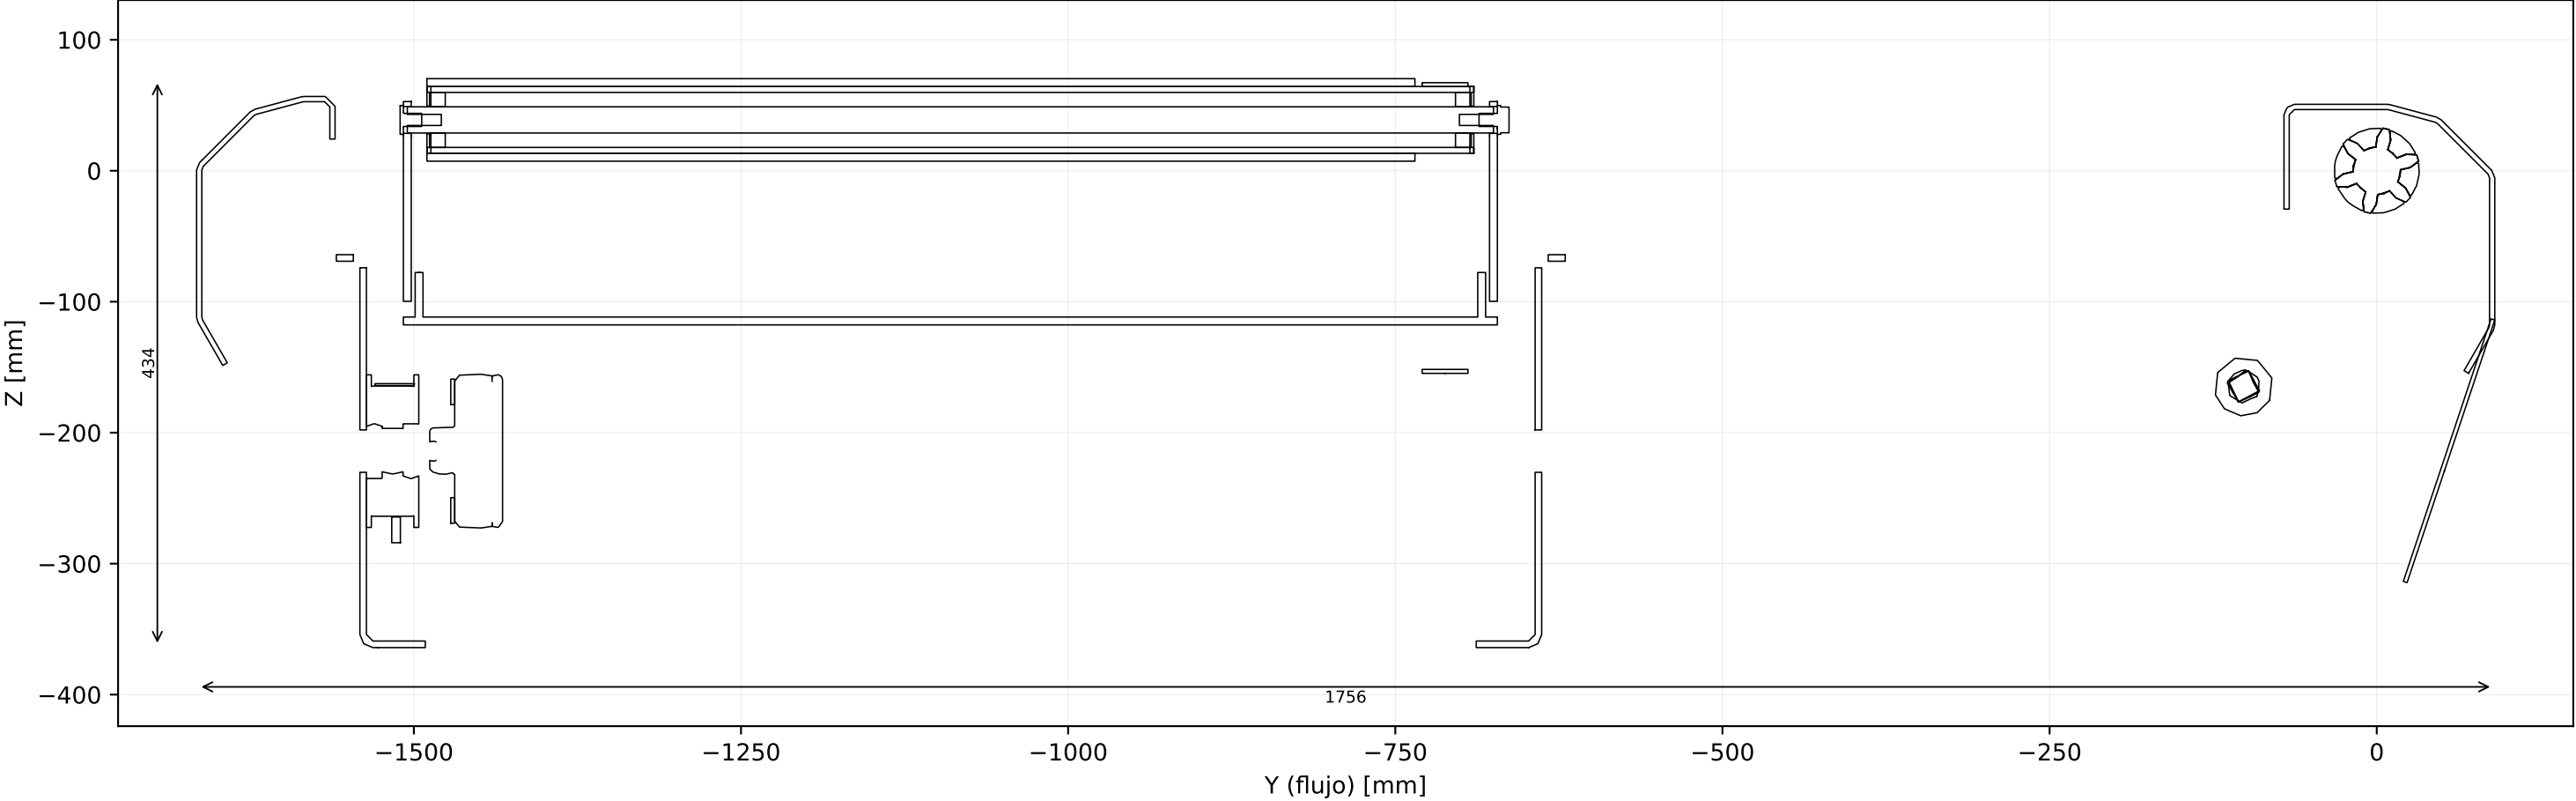



foto3d

SORTER REAL (sorter_CO.stp) + Transferencia 90°

Corte longitudinal A-A (plano X=208, eje de máquina)

Escala 1:10 · mm · 2026-07-20

Corte transversal B-B (plano Y=-1090, por la transferencia)

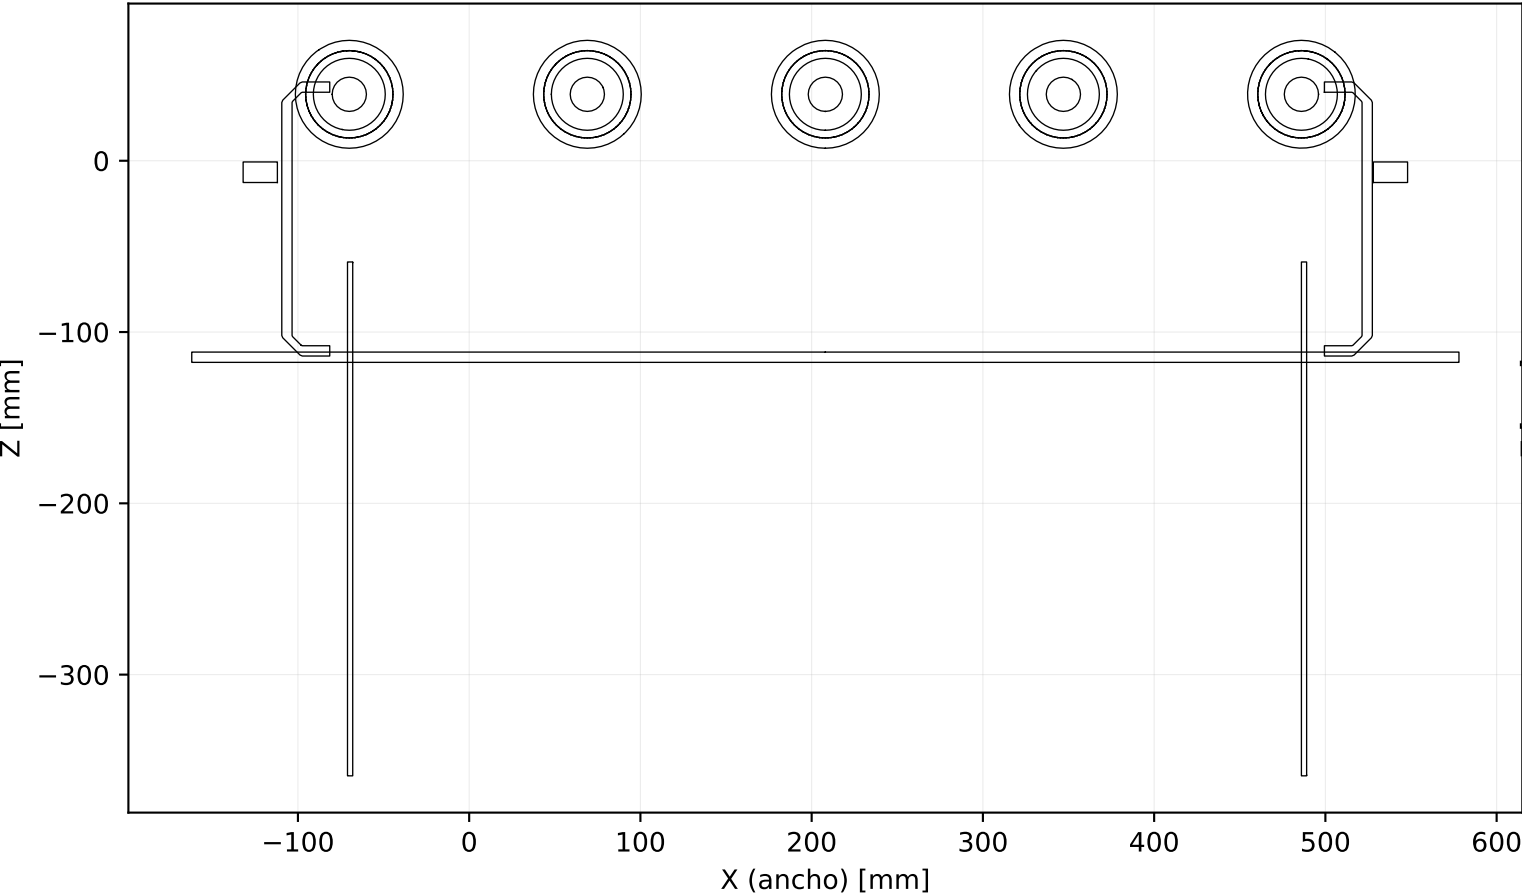

Corte transversal C-C (plano Y=-300, por cabezal motriz)

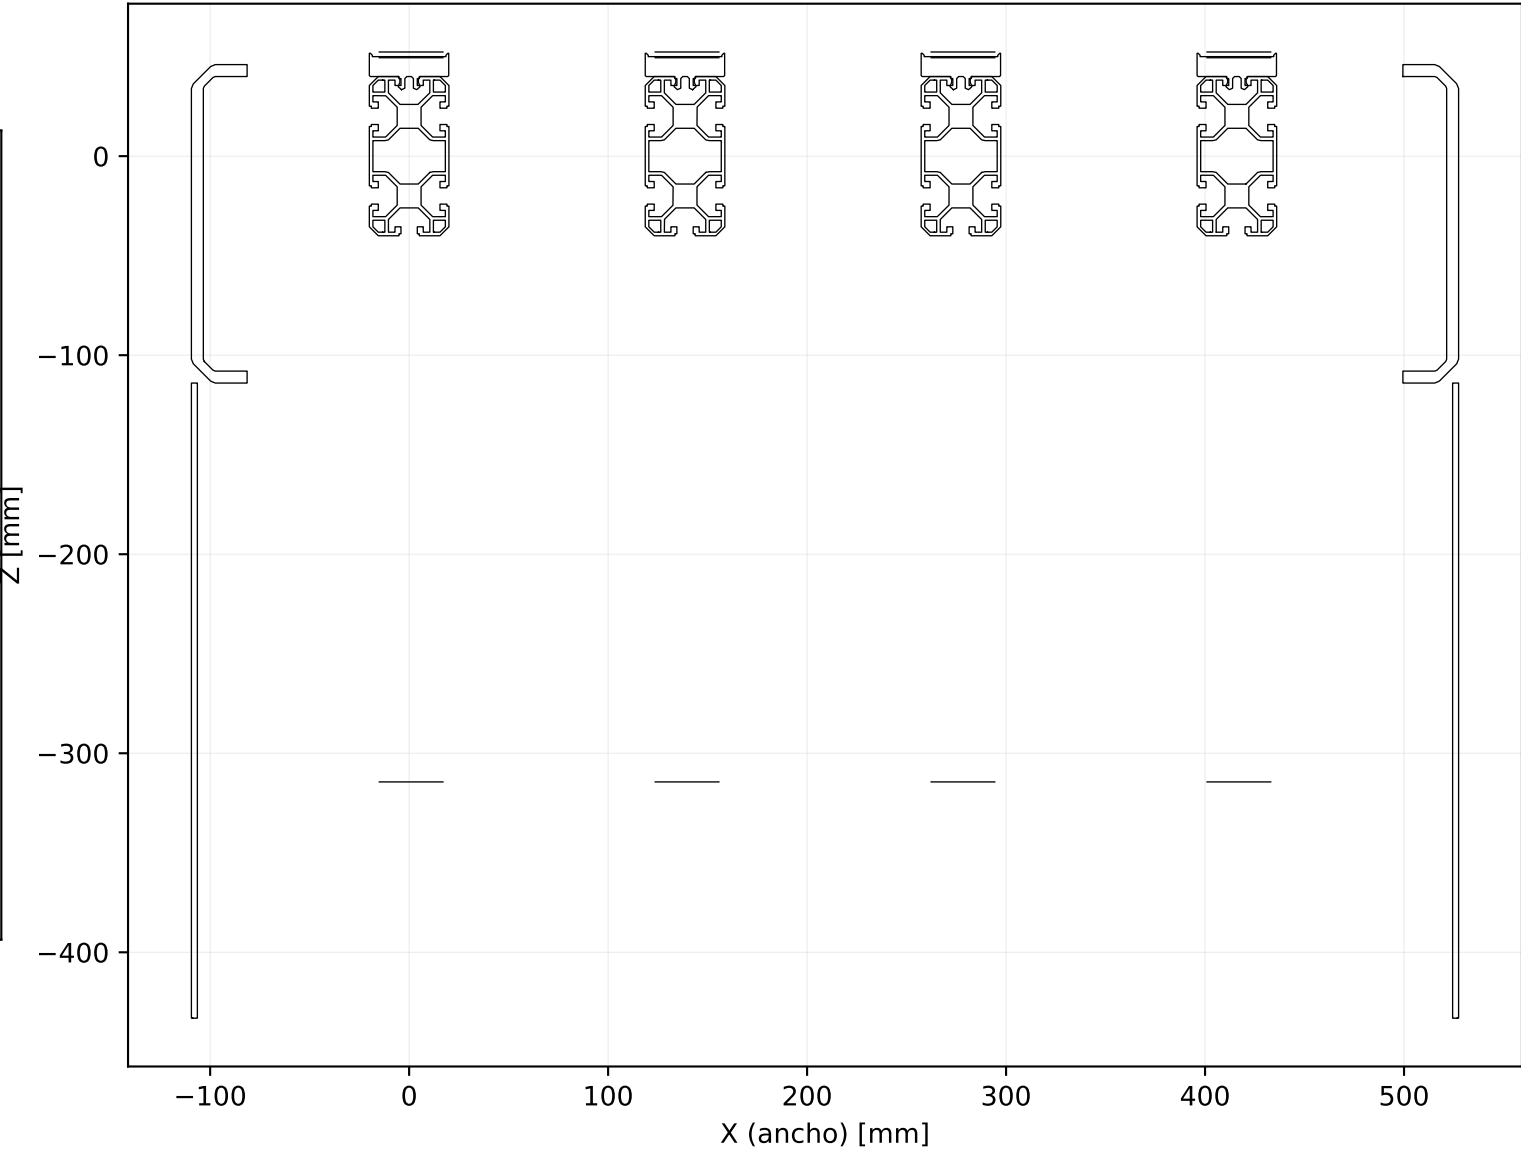


foto3d

SORTER REAL (sorter_CO.stp) + Transferencia 90°

Cortes transversales B-B y C-C

Escala 1:10 · mm · 2026-07-20